



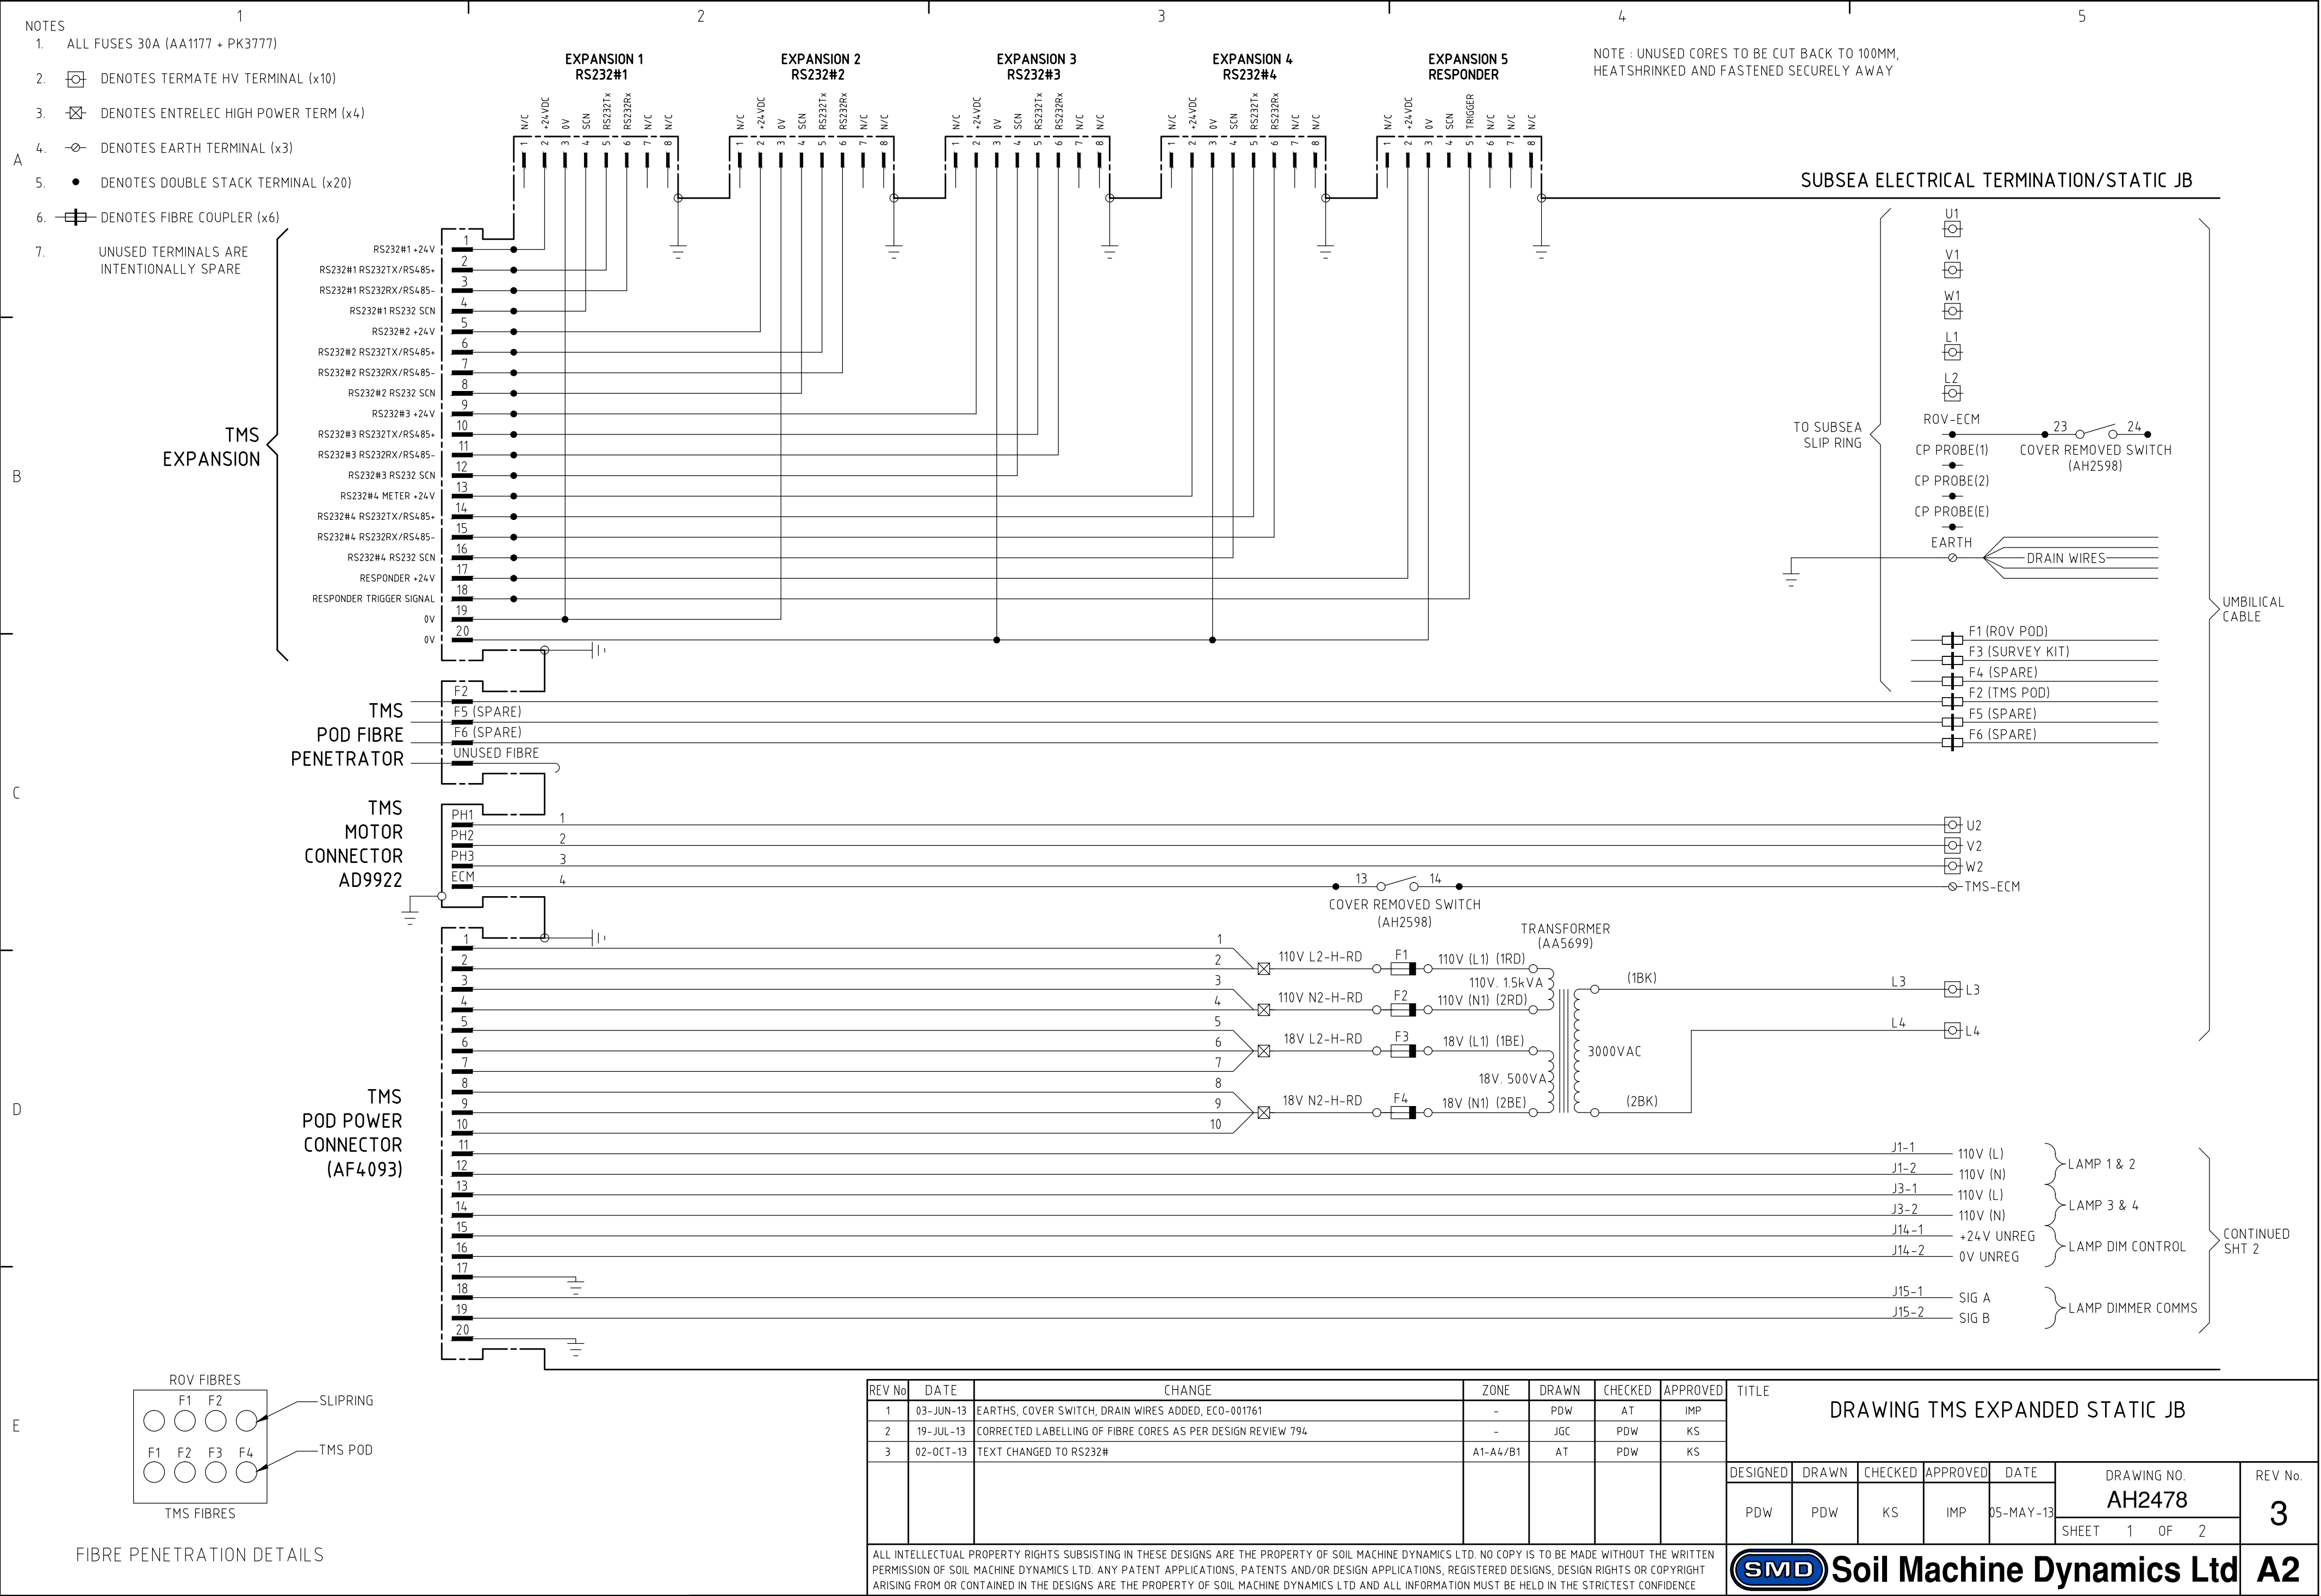

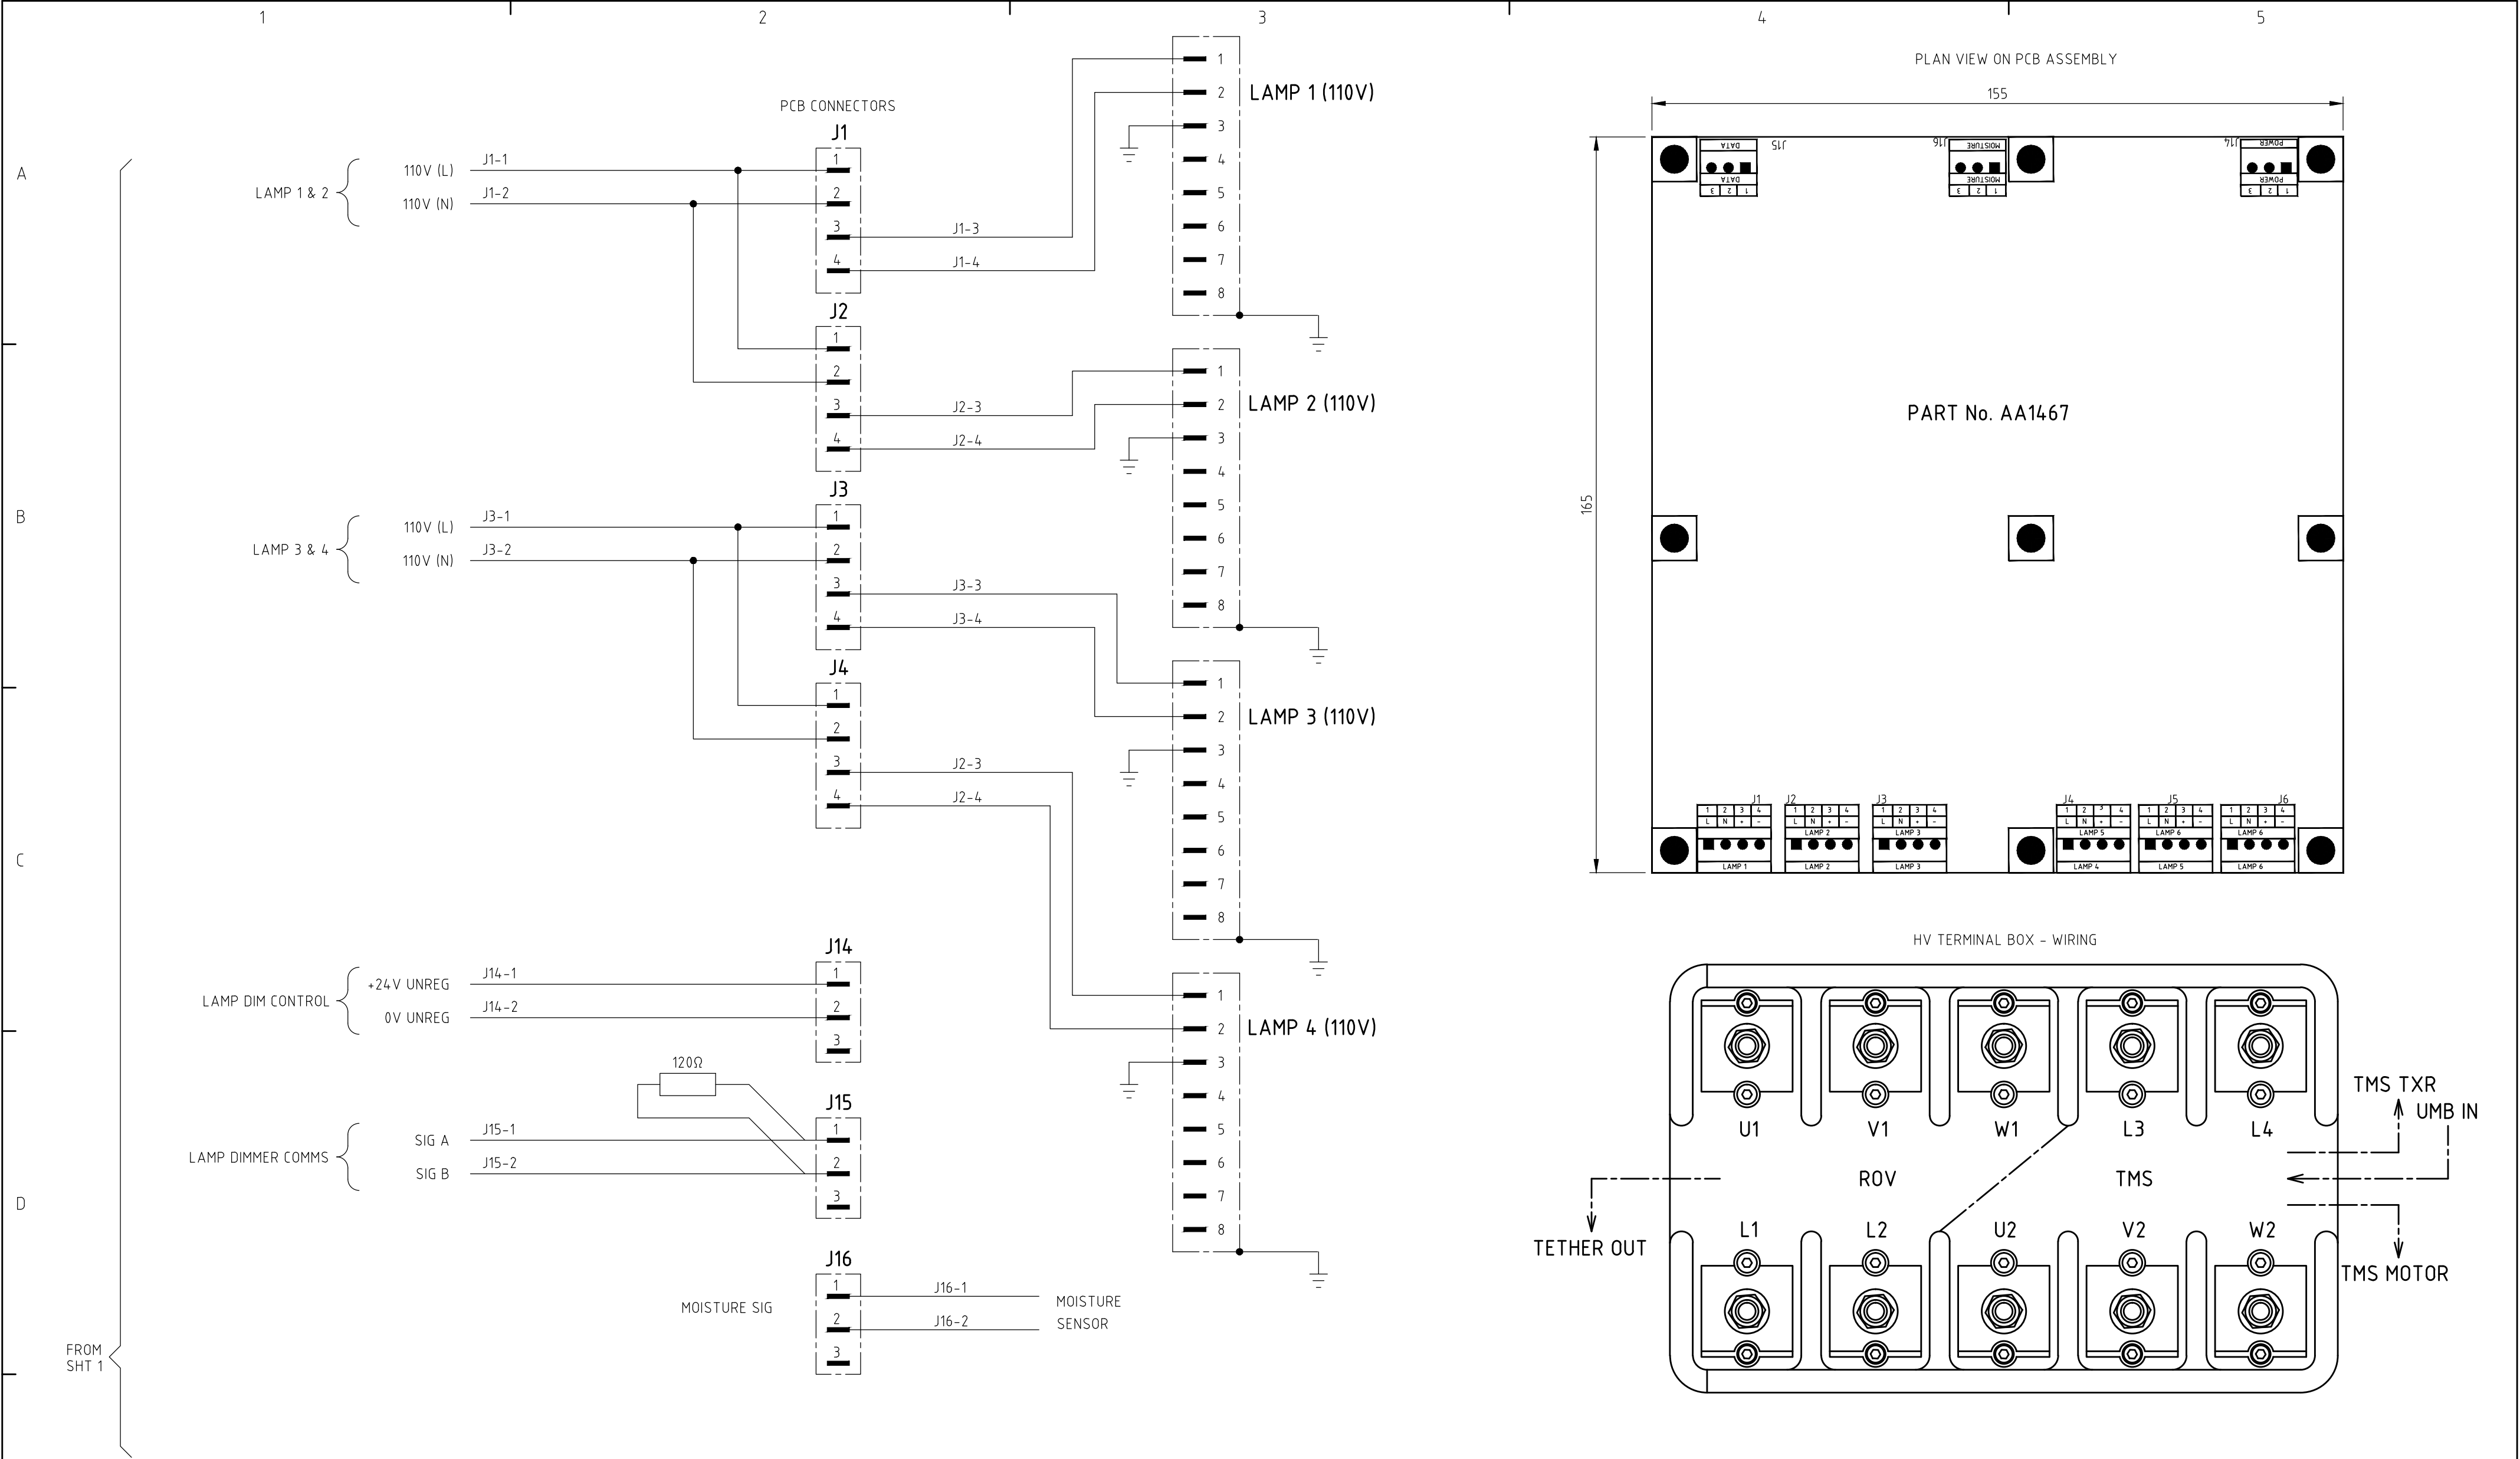

REV No	DATE	CHANGE	ZONE	DRAWN	CHECKED	APPROVED	TITLE							
1	03-JUN-13	HV TERMINAL BOX CONNECTIONS ADDED, ECO-001761	-	PDW	AT	IMP	DRAWING TMS EXPANDED STATIC JB							
2	19-JUL-13	NO CHANGE TO THIS SHEET	-	JGC	PDW	KS								
3	02-OCT-13	NO CHANGE TO THIS SHEET	-	AT	PDW	KS								
							DESIGNED	DRAWN	CHECKED	APPROVED	DATE	DRAWING NO.		REV No.
							PDW	PDW	KS	IMP	05-MAY-13	AH2478		
												SHEET 2 OF 2		
ALL INTELLECTUAL PROPERTY RIGHTS SUBSISTING IN THESE DESIGNS ARE THE PROPERTY OF SOIL MACHINE DYNAMICS LTD. NO COPY IS TO BE MADE WITHOUT THE WRITTEN PERMISSION OF SOIL MACHINE DYNAMICS LTD. ANY PATENT APPLICATIONS, PATENTS AND/OR DESIGN APPLICATIONS, REGISTERED DESIGNS, DESIGN RIGHTS OR COPYRIGHT ARISING FROM OR CONTAINED IN THE DESIGNS ARE THE PROPERTY OF SOIL MACHINE DYNAMICS LTD AND ALL INFORMATION MUST BE HELD IN THE STRICTEST CONFIDENCE							 Soil Machine Dynamics Ltd A2							