

1

2

3

4

5

A

B

C

D

E

LV POWER DISTRIBUTION UNIT (PDU) PANEL

SHT.No	DESCRIPTION
1	FRONT SHEET
2	INCOMING, ROV POD & MOTOR SUPPLIES
3	TMS POD & MOTOR SUPPLIES, 110V & 240V AC SUPPLIES
4	110V AC CONTROL & PSU's
5	24V DC CONTROL CIRCUITS
6	24V DC CONTROL CIRCUITS
7	PLC DIGITAL INPUTS
8	PLC DIGITAL OUTPUTS
9	PLC ANALOGUE INPUTS
10	EXTERNAL TERMINATIONS
11	OVERALL CONTROL CABIN EARTHING DIAGRAM
12	
13	
14	
15	

NOTES

1. FOR INTERCONNECTING MULTICORE CABLE NUMBER AND CORE NUMBER SEE SHEET 10.

2. ALL WIRING TO BE 0.5mm - TRI-RATED - TYPE B - UNLESS OTHERWISE STATED.

3. WIRE NUMBERS ALLOCATED TO THIS DRAWING (& AH2646) ARE 1 TO 599, LAST WIRE NUMBER USED 576.
UNUSED WIRE Nos. ARE 51, 55-60, 63-66, 70-75, 78, 79, 84, 99, 113, 132-149, 166-199, 210-213, 219-222, 226-229, 234-299, 304, 307, 314-319, 346, 351-354, 357, 360-362, 367-500, 505, 506, 516, 521, 522, 529-532, 551-556, 577-599.

4. WIRE NUMBERS OTHER THAN ABOVE ARE DERIVED FROM OTHER SHEETS.

5. ALL FUSES ARE TYPE 'T' TIME DELAY.

6. ALL CABLES TO BE IN ACCORDANCE WITH SMD DRG.No.PD0739 ISS. 7.

7. LAST FUSE NUMBER USED F31. LAST MCB NUMBER USED Q23. LAST RELAY NUMBER USED K12.


8. ALL EQUIPMENT IS MOUNTED IN LV PDU PANEL.
(HV TRANSFORMERS ARE MOUNTED IN SEPARATE ENCLOSURE, SEE DRAWING AH2646)


9. ECM TIMERS (TR1 & TR2) SET TO 3 SECONDS AS FOLLOWS :-

TOP DIAL - 0.3
MIDDLE DIAL - S 10
BOTTOM DIAL - R


10. DISPLAYED VOLTAGE TO BE SCALED TO GIVE CORRECT.

REV No	DATE	CHANGE	ZONE	DRAWN	CHECKED	APPROVED	TITLE						
1	07 aug 13	NO CHANGE THIS SHEET	B2	K.S.	A.T.	I.M.P.	DRAWING LV PDU WIRING FRONT SHEET						
2	30 SEP 13	AS COMMISSIONED	ALL	K.S.	A.T.	I.M.P.							
3	20 JAN 14	NOTE 10 ADDED	C3	K.S.	A.T.	I.M.P.							
							DESIGNED	DRAWN	CHECKED	APPROVED	DATE	DRAWING NO.	REV No.
							KS	W.R.	A.T.	I.M.P.	15MAY2013	AH2645	3
												SHEET 1 OF 11	
ALL INTELLECTUAL PROPERTY RIGHTS SUBSISTING IN THESE DESIGNS ARE THE PROPERTY OF SOIL MACHINE DYNAMICS LTD. NO COPY IS TO BE MADE WITHOUT THE WRITTEN PERMISSION OF SOIL MACHINE DYNAMICS LTD. ANY PATENT APPLICATIONS, PATENTS AND/OR DESIGN APPLICATIONS, REGISTERED DESIGNS, DESIGN RIGHTS OR COPYRIGHT ARISING FROM OR CONTAINED IN THE DESIGNS ARE THE PROPERTY OF SOIL MACHINE DYNAMICS LTD AND ALL INFORMATION MUST BE HELD IN THE STRICTEST CONFIDENCE							 Soil Machine Dynamics Ltd					A2	

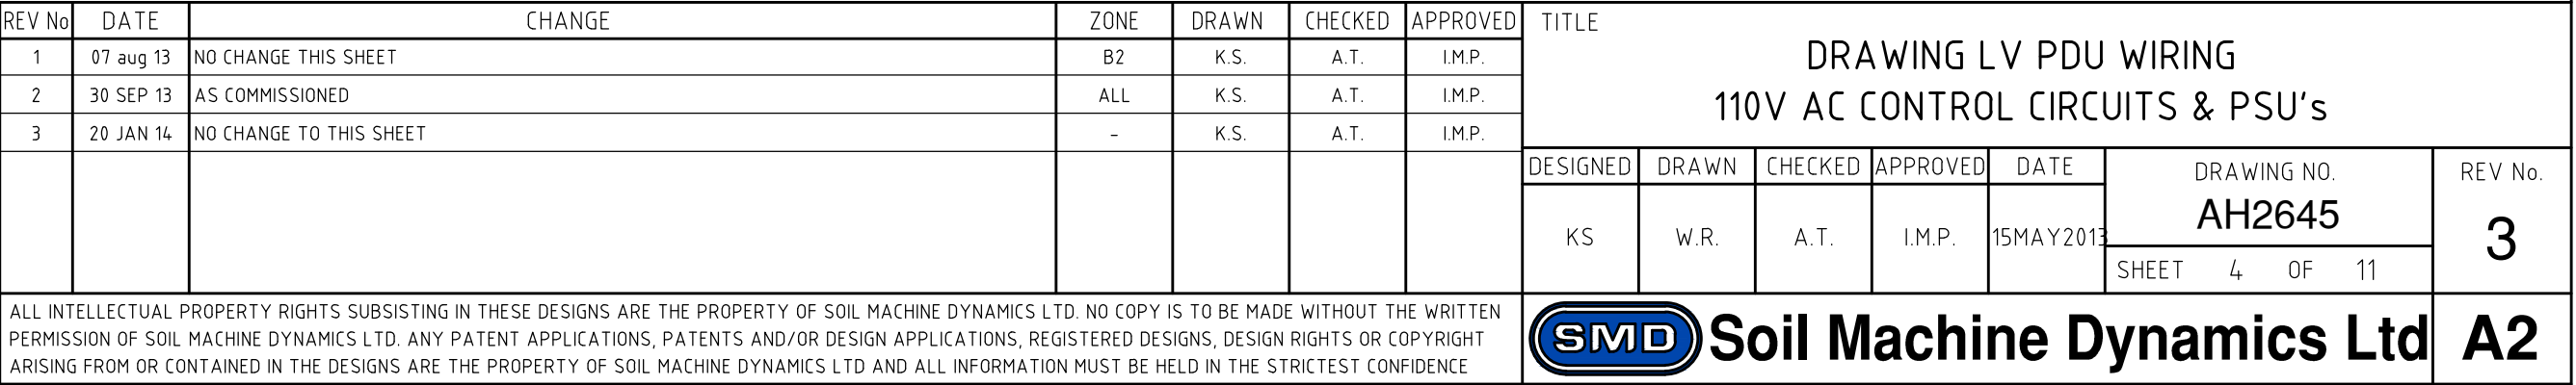






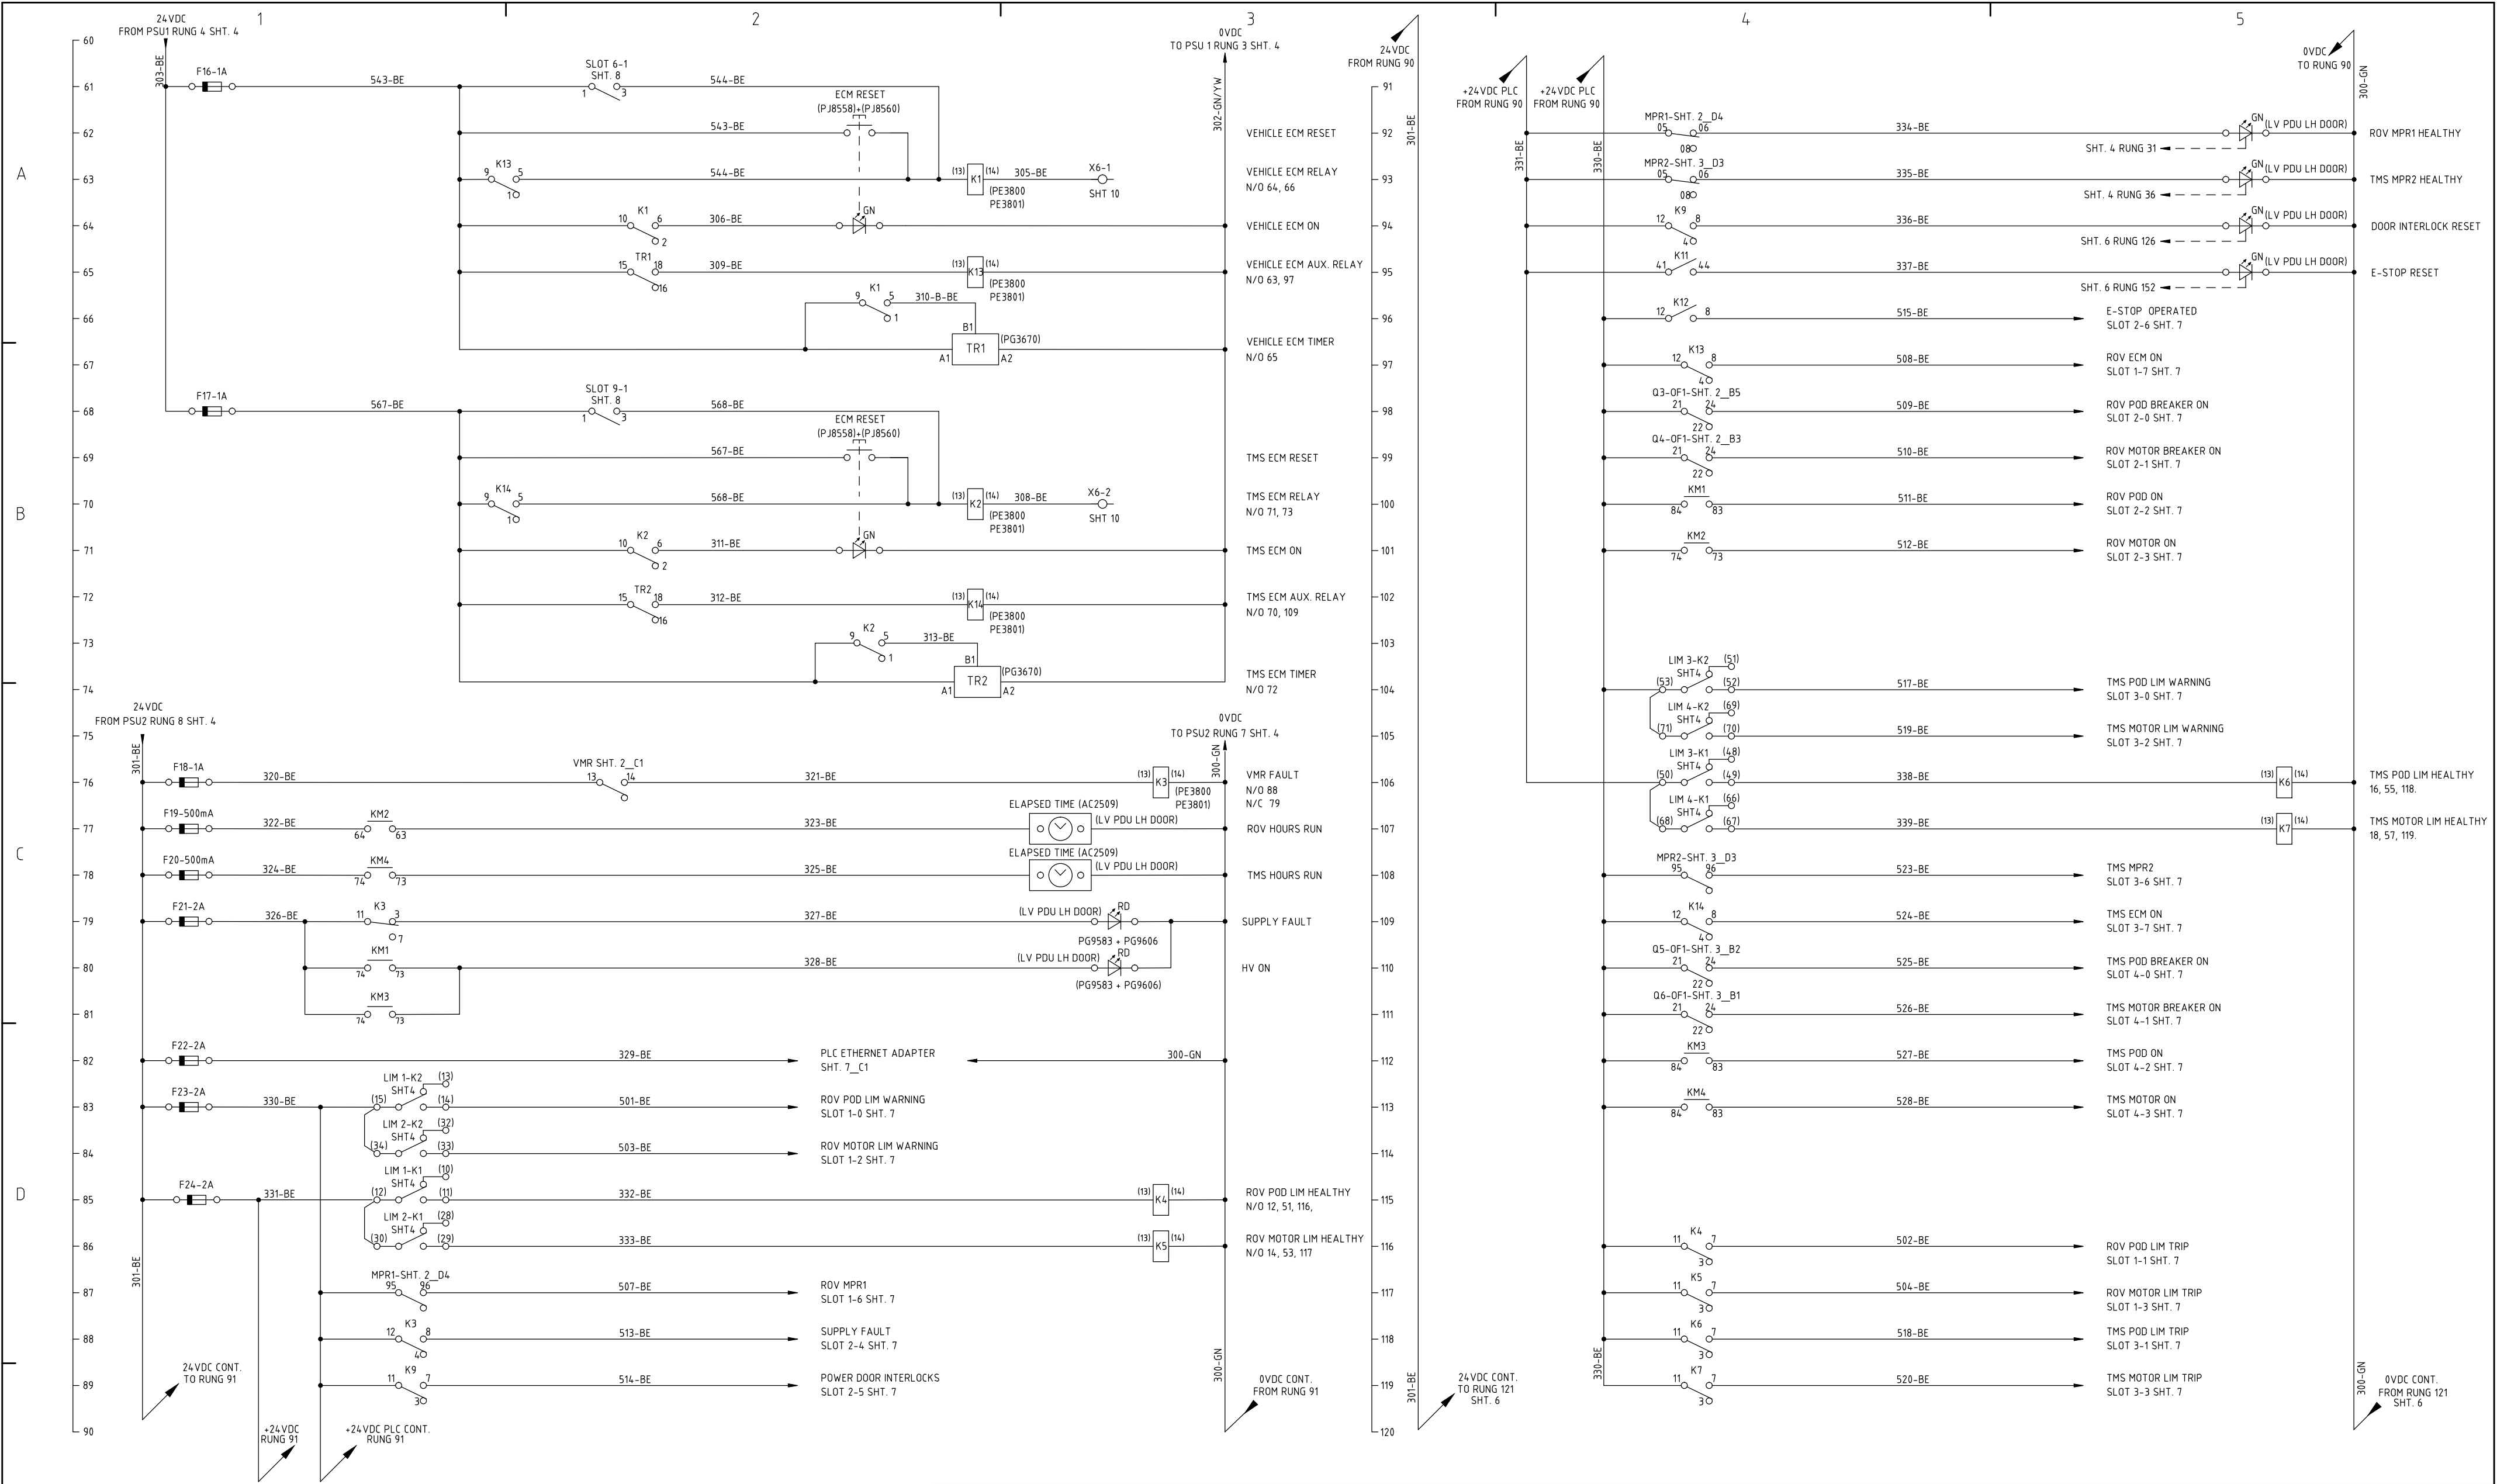


REV No	DATE	CHANGE	ZONE	DRAWN	CHECKED	APPROVED	TITLE						
1	07 aug 13	NO CHANGE THIS SHEET	B2	K.S.	A.T.	I.M.P.	DRAWING LV PDU WIRING 24V DC CONTROL CIRCUITS						
2	30 SEP 13	AS COMMISSIONED	ALL	K.S.	A.T.	I.M.P.							
3	20 JAN 14	NO CHANGE TO THIS SHEET	-	K.S.	A.T.	I.M.P.							
							DESIGNED	DRAWN	CHECKED	APPROVED	DATE	DRAWING NO.	REV No.
							KS	W.R.	A.T.	I.M.P.	15MAY2013	AH2645	3
							SHEET 5 OF 11						
ALL INTELLECTUAL PROPERTY RIGHTS SUBSISTING IN THESE DESIGNS ARE THE PROPERTY OF SOIL MACHINE DYNAMICS LTD. NO COPY IS TO BE MADE WITHOUT THE WRITTEN PERMISSION OF SOIL MACHINE DYNAMICS LTD. ANY PATENT APPLICATIONS, PATENTS AND/OR DESIGN APPLICATIONS, REGISTERED DESIGNS, DESIGN RIGHTS OR COPYRIGHT ARISING FROM OR CONTAINED IN THE DESIGNS ARE THE PROPERTY OF SOIL MACHINE DYNAMICS LTD AND ALL INFORMATION MUST BE HELD IN THE STRICTEST CONFIDENCE							 Soil Machine Dynamics Ltd						A2

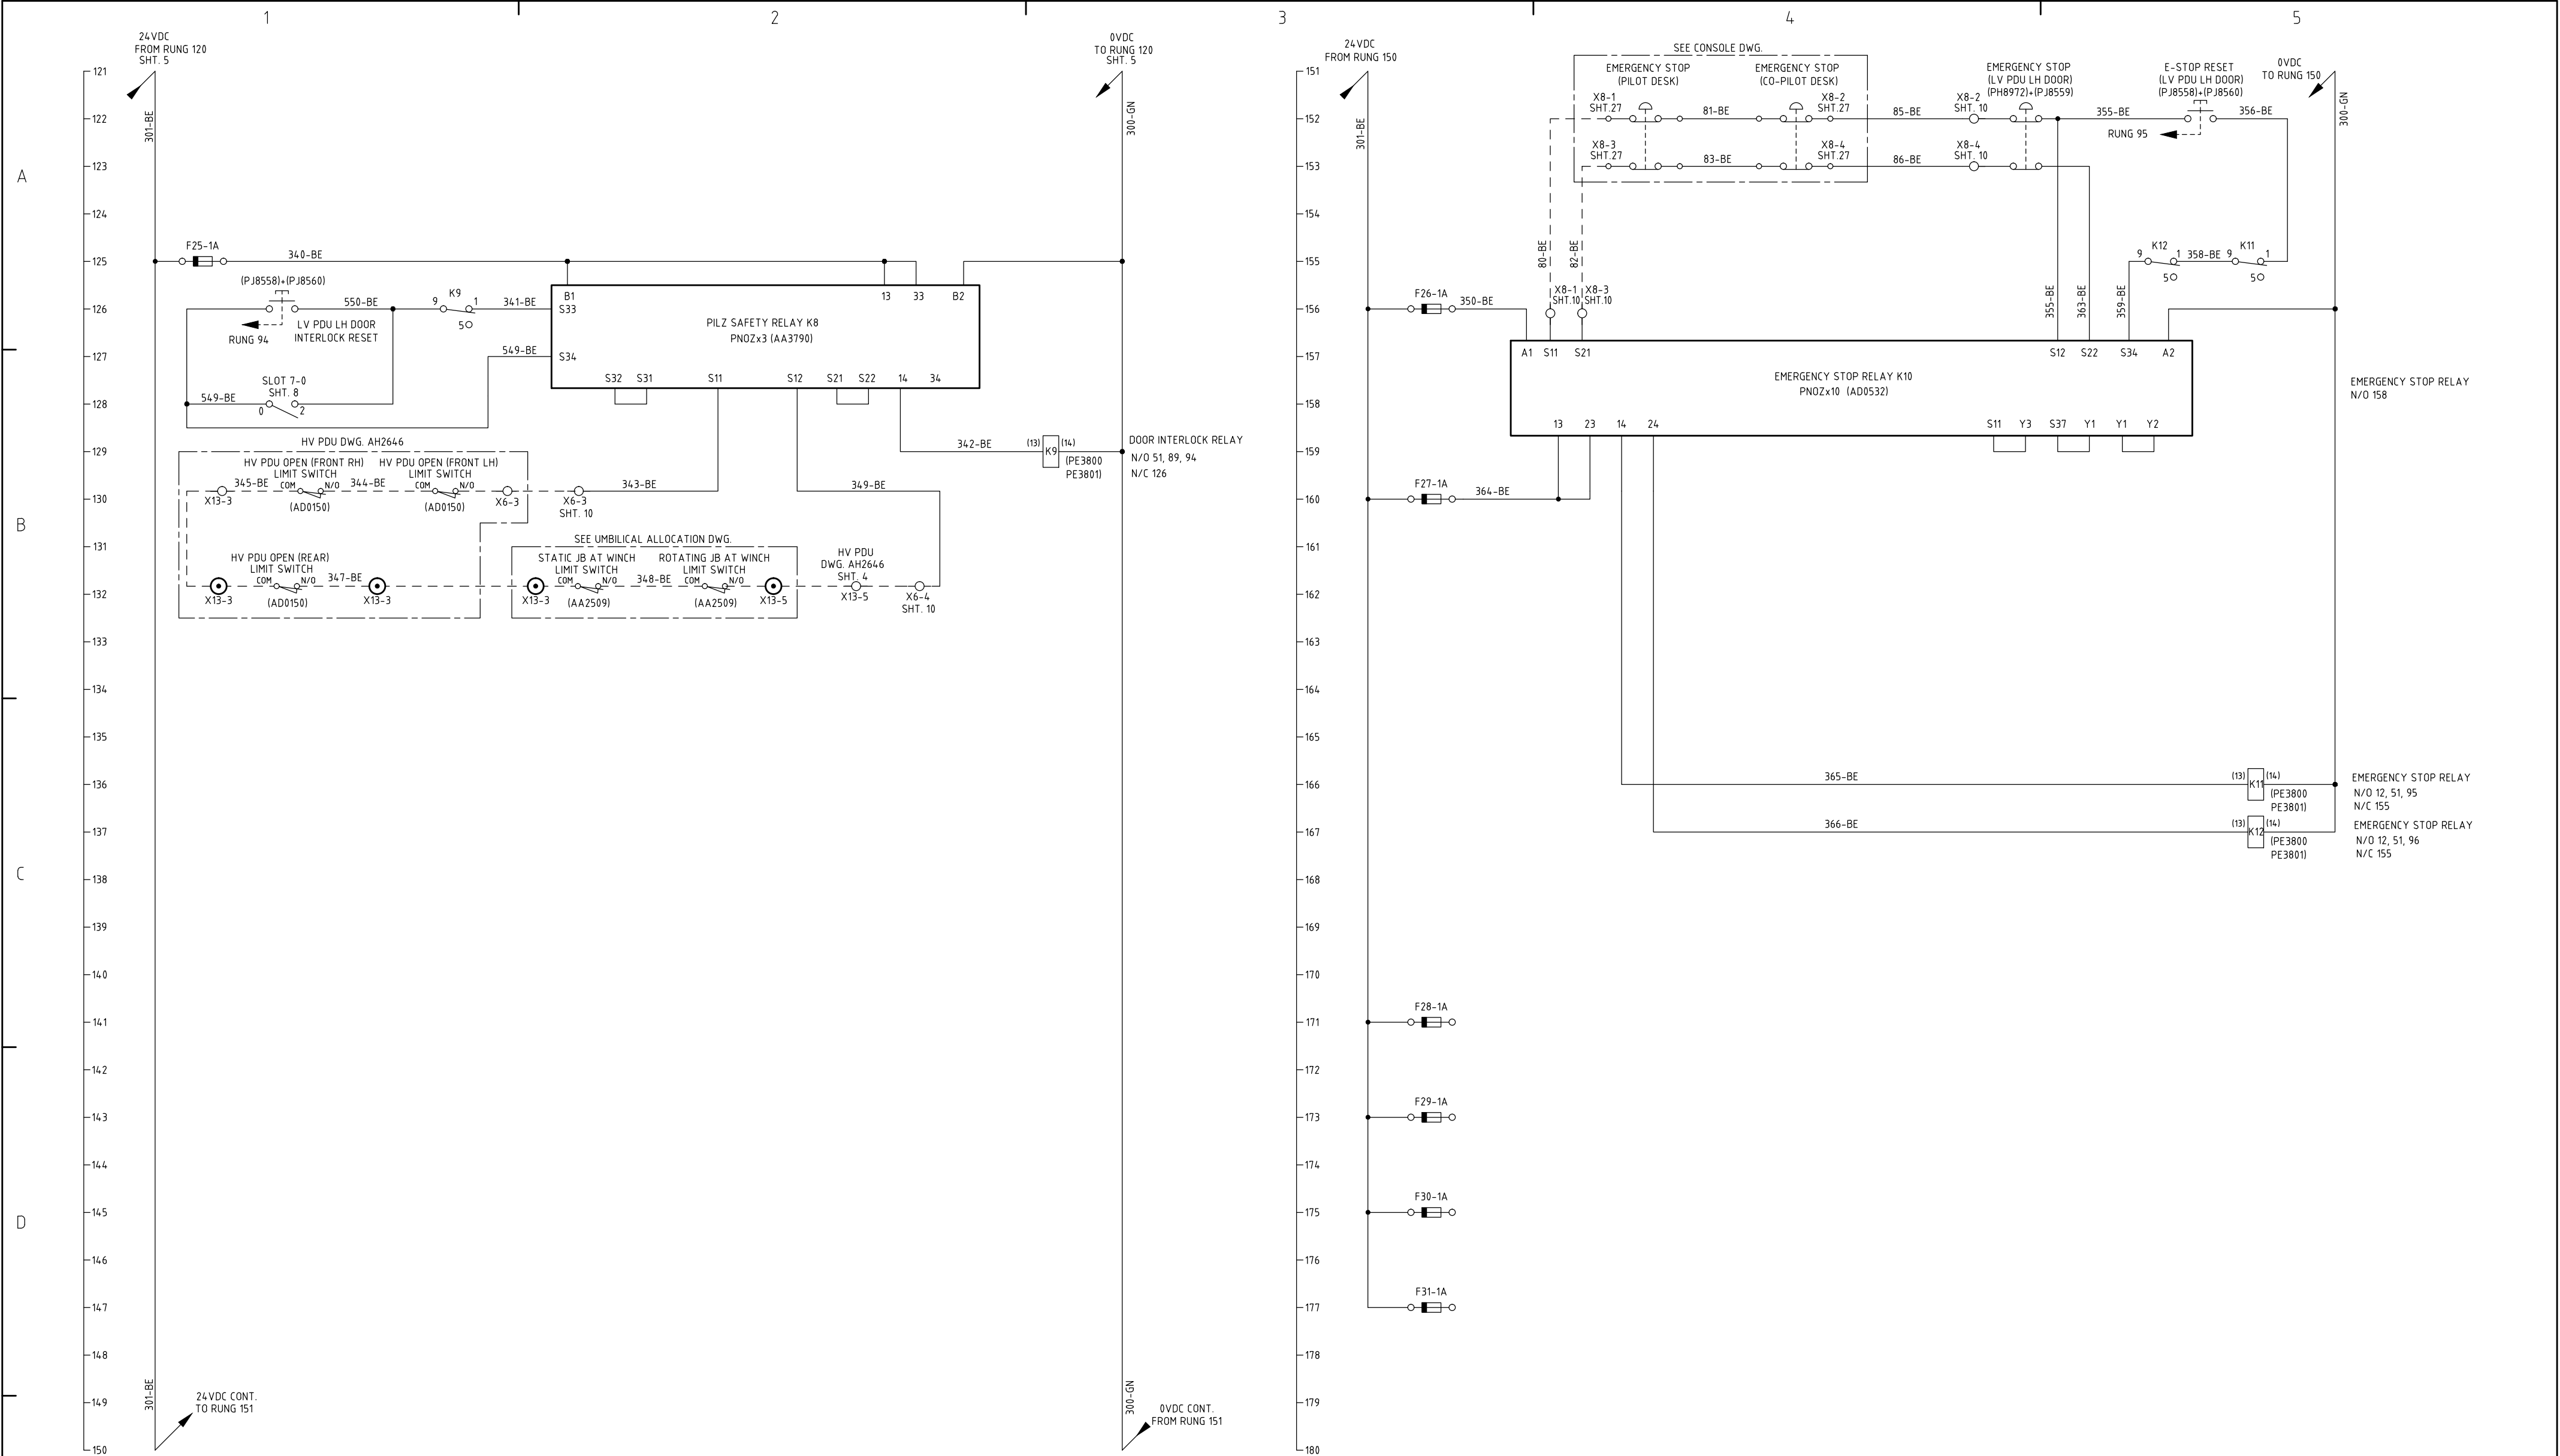

REV No	DATE	CHANGE	ZONE	DRAWN	CHECKED	APPROVED	TITLE							
1	07 aug 13	NO CHANGE THIS SHEET	B2	K.S.	A.T.	I.M.P.	DRAWING LV PDU WIRING 24V DC CONTROL CIRCUITS							
2	30 SEP 13	AS COMMISSIONED	ALL	K.S.	A.T.	I.M.P.								
3	20 JAN 14	NO CHANGE TO THIS SHEET	-	K.S.	A.T.	I.M.P.								
							DESIGNED	DRAWN	CHECKED	APPROVED	DATE	DRAWING NO. AH2645		REV No. 3
							KS	W.R.	A.T.	I.M.P.	15MAY2013	SHEET 6 OF 11		
ALL INTELLECTUAL PROPERTY RIGHTS SUBSISTING IN THESE DESIGNS ARE THE PROPERTY OF SOIL MACHINE DYNAMICS LTD. NO COPY IS TO BE MADE WITHOUT THE WRITTEN PERMISSION OF SOIL MACHINE DYNAMICS LTD. ANY PATENT APPLICATIONS, PATENTS AND/OR DESIGN APPLICATIONS, REGISTERED DESIGNS, DESIGN RIGHTS OR COPYRIGHT ARISING FROM OR CONTAINED IN THE DESIGNS ARE THE PROPERTY OF SOIL MACHINE DYNAMICS LTD AND ALL INFORMATION MUST BE HELD IN THE STRICTEST CONFIDENCE							 Soil Machine Dynamics Ltd							A2

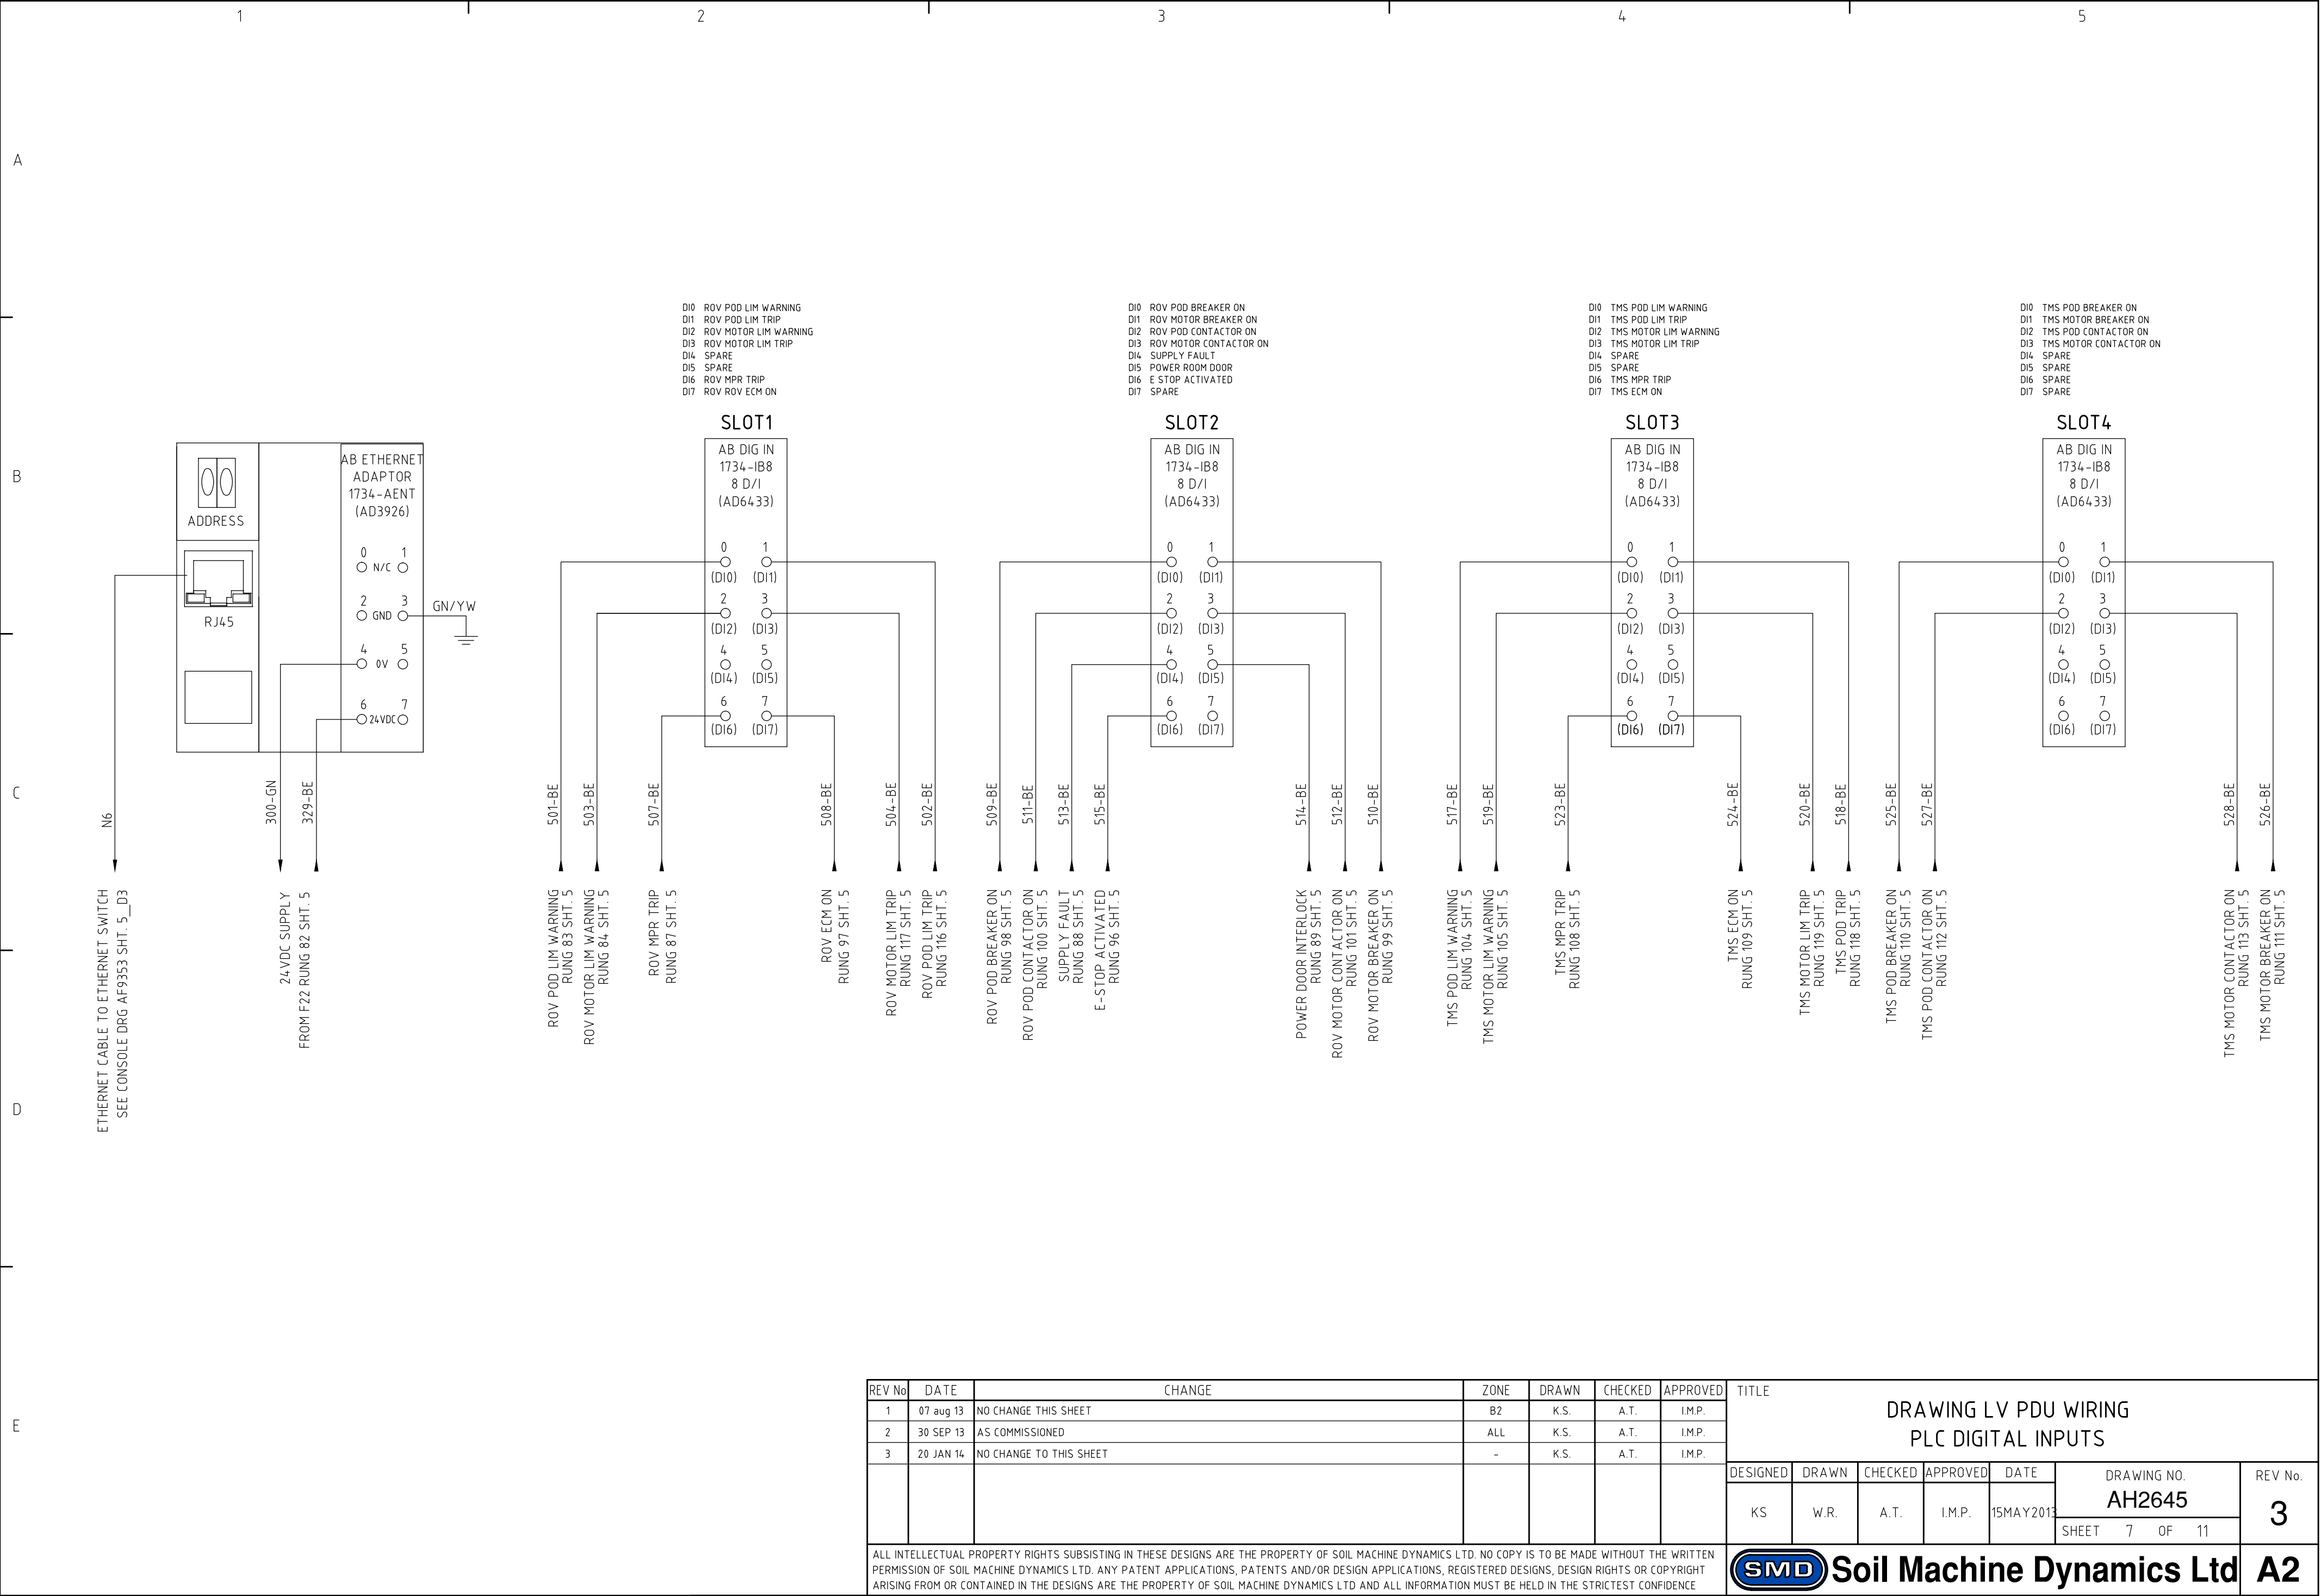

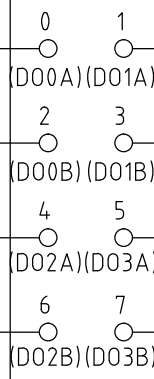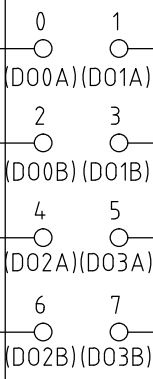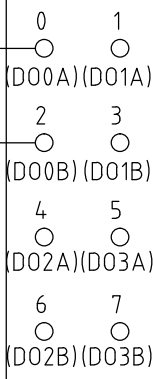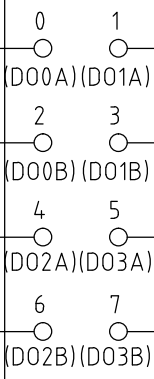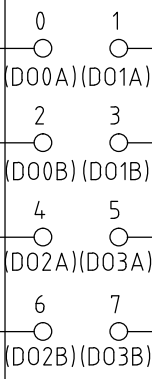

12345



A

B


C

D

E

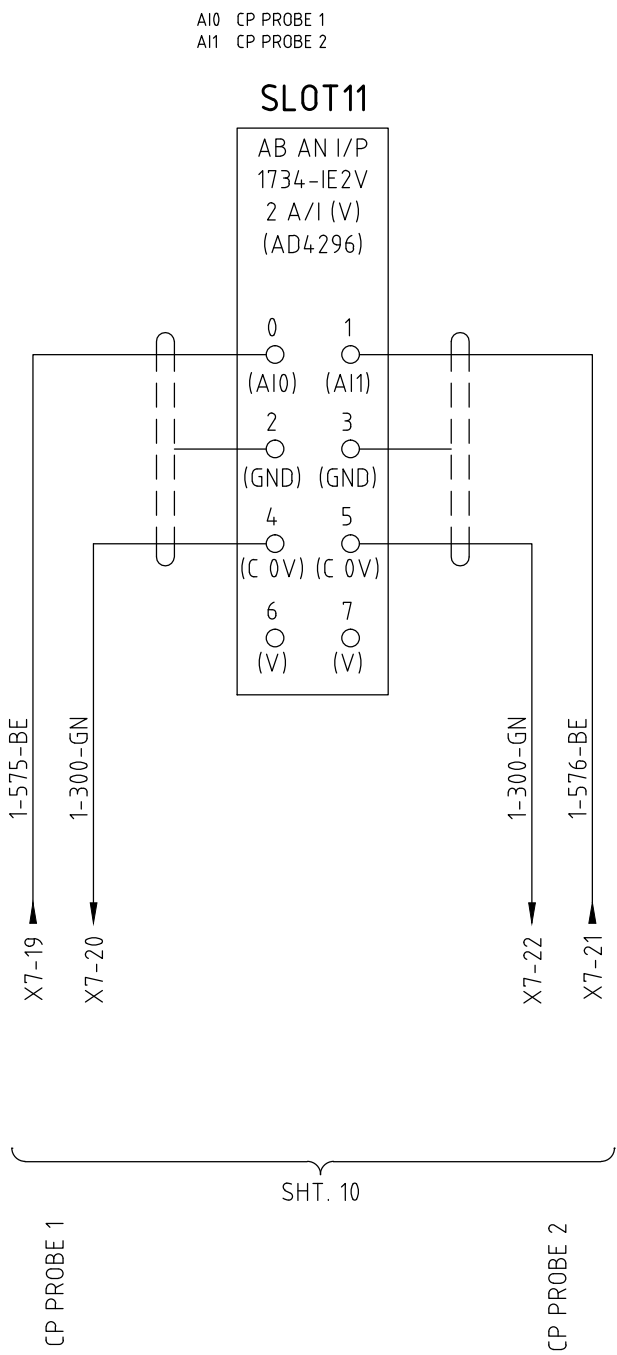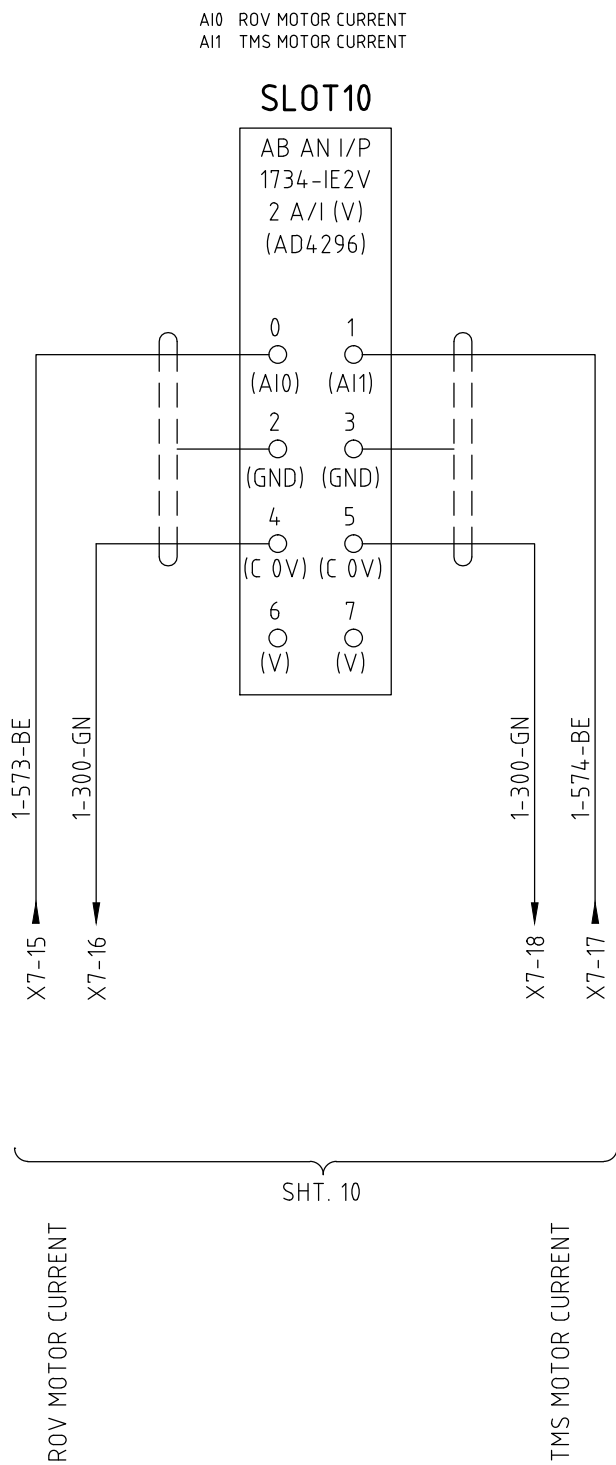

REV No	DATE	CHANGE	ZONE	DRAWN	CHECKED	APPROVED	TITLE							
1	07 aug 13	NO CHANGE THIS SHEET	B2	K.S.	A.T.	I.M.P.	DRAWING LV PDU WIRING PLC ANALOGUE INPUTS							
2	30 SEP 13	AS COMMISSIONED	ALL	K.S.	A.T.	I.M.P.								
3	20 JAN 14	NO CHANGE TO THIS SHEET	-	K.S.	A.T.	I.M.P.								
							DESIGNED	DRAWN	CHECKED	APPROVED	DATE	DRAWING NO. AH2645		REV No. 3
							KS	W.R.	A.T.	I.M.P.	15MAY2013	SHEET 9 OF 11		
ALL INTELLECTUAL PROPERTY RIGHTS SUBSISTING IN THESE DESIGNS ARE THE PROPERTY OF SOIL MACHINE DYNAMICS LTD. NO COPY IS TO BE MADE WITHOUT THE WRITTEN PERMISSION OF SOIL MACHINE DYNAMICS LTD. ANY PATENT APPLICATIONS, PATENTS AND/OR DESIGN APPLICATIONS, REGISTERED DESIGNS, DESIGN RIGHTS OR COPYRIGHT ARISING FROM OR CONTAINED IN THE DESIGNS ARE THE PROPERTY OF SOIL MACHINE DYNAMICS LTD AND ALL INFORMATION MUST BE HELD IN THE STRICTEST CONFIDENCE							 Soil Machine Dynamics Ltd							A2

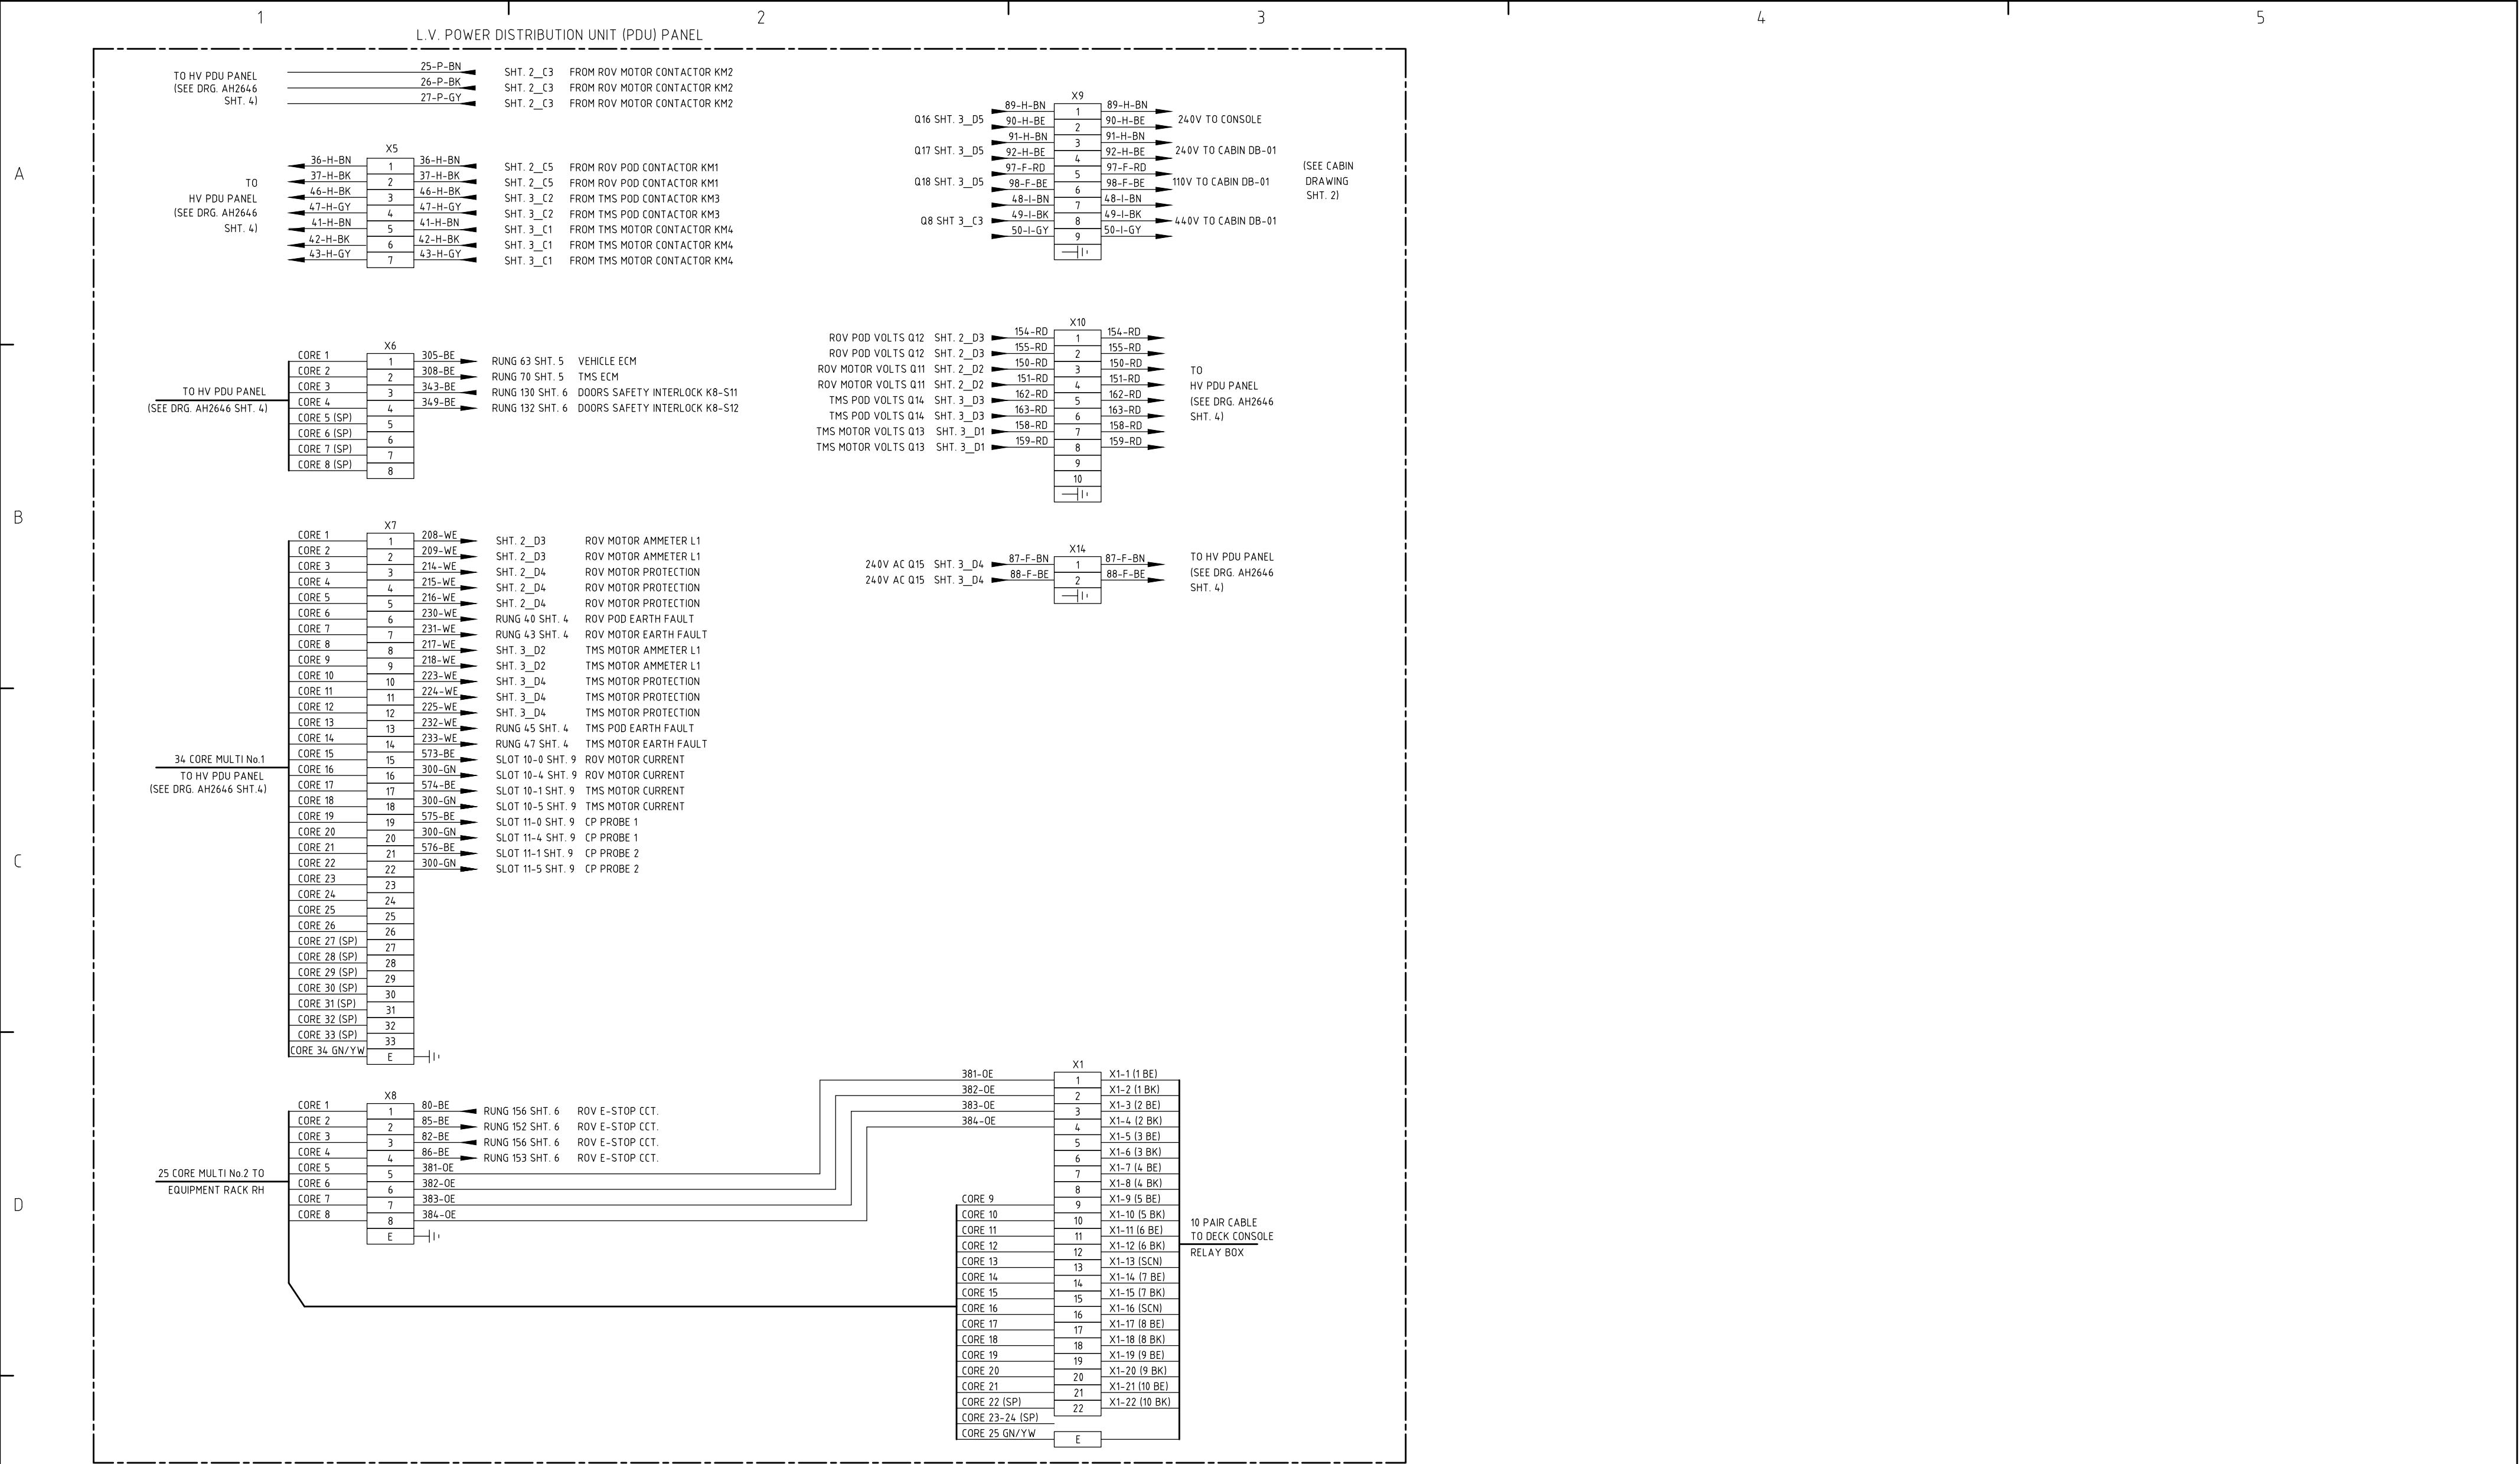

REV No	DATE	CHANGE	ZONE	DRAWN	CHECKED	APPROVED	TITLE						
1	07 aug 13	WIRES 36 & 37 COLOURS CORRECTED.	B2	K.S.	A.T.	I.M.P.	DRAWING LV PDU WIRING EXTERNAL TERMINATIONS						
2	30 SEP 13	AS COMMISSIONED	ALL	K.S.	A.T.	I.M.P.							
3	20 JAN 14	NO CHANGE TO THIS SHEET	-	K.S.	A.T.	I.M.P.							
							DESIGNED	DRAWN	CHECKED	APPROVED	DATE	DRAWING NO.	REV No.
							KS	W.R.	A.T.	I.M.P.	15MAY2013	AH2645	3
												SHEET 10 OF 11	
ALL INTELLECTUAL PROPERTY RIGHTS SUBSISTING IN THESE DESIGNS ARE THE PROPERTY OF SOIL MACHINE DYNAMICS LTD. NO COPY IS TO BE MADE WITHOUT THE WRITTEN PERMISSION OF SOIL MACHINE DYNAMICS LTD. ANY PATENT APPLICATIONS, PATENTS AND/OR DESIGN APPLICATIONS, REGISTERED DESIGNS, DESIGN RIGHTS OR COPYRIGHT ARISING FROM OR CONTAINED IN THE DESIGNS ARE THE PROPERTY OF SOIL MACHINE DYNAMICS LTD AND ALL INFORMATION MUST BE HELD IN THE STRICTEST CONFIDENCE							 Soil Machine Dynamics Ltd						A2

