


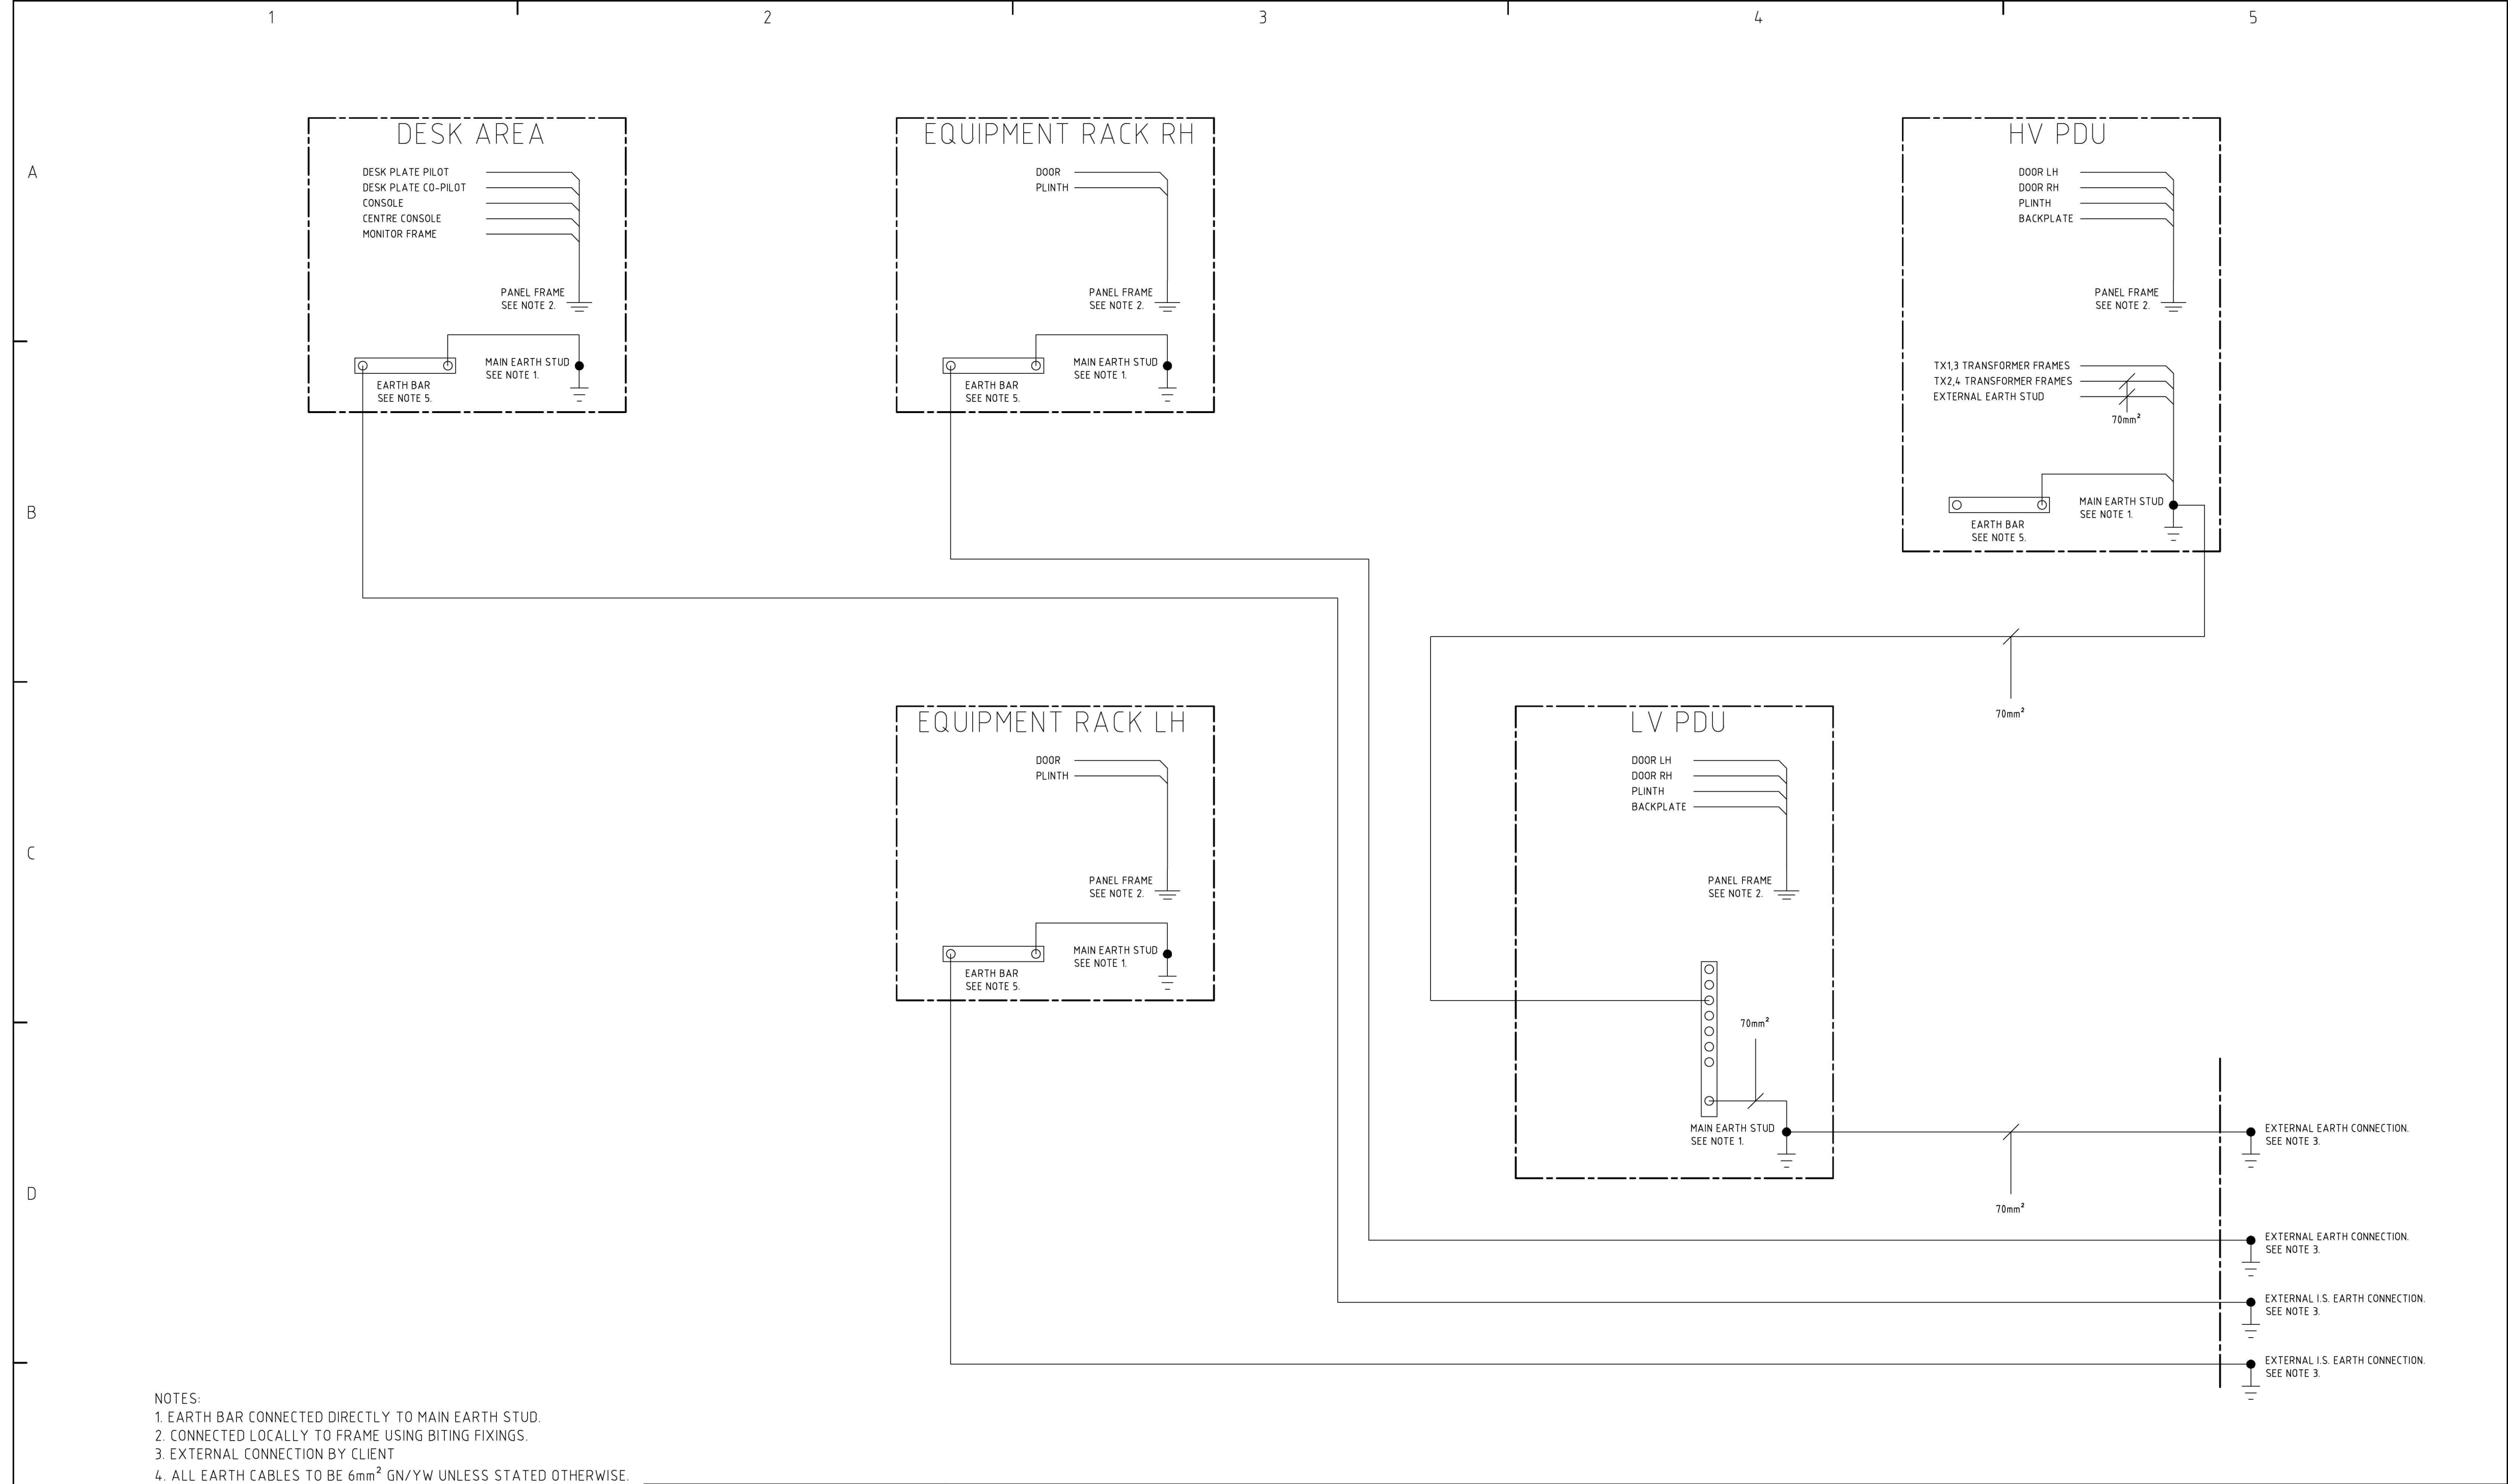

NOTES:
1. EARTH BAR CONNECTED DIRECTLY TO MAIN EARTH STUD.
2. CONNECTED LOCALLY TO FRAME USING BITING FIXINGS.
3. EXTERNAL CONNECTION BY CLIENT
4. ALL EARTH CABLES TO BE 6mm² GN/YW UNLESS STATED OTHERWISE.
5. EARTH BAR CONSISTS OF:
COPPER BAR 215x13x6 (AE1524), MOUNTING BRACKETS (AE1525)